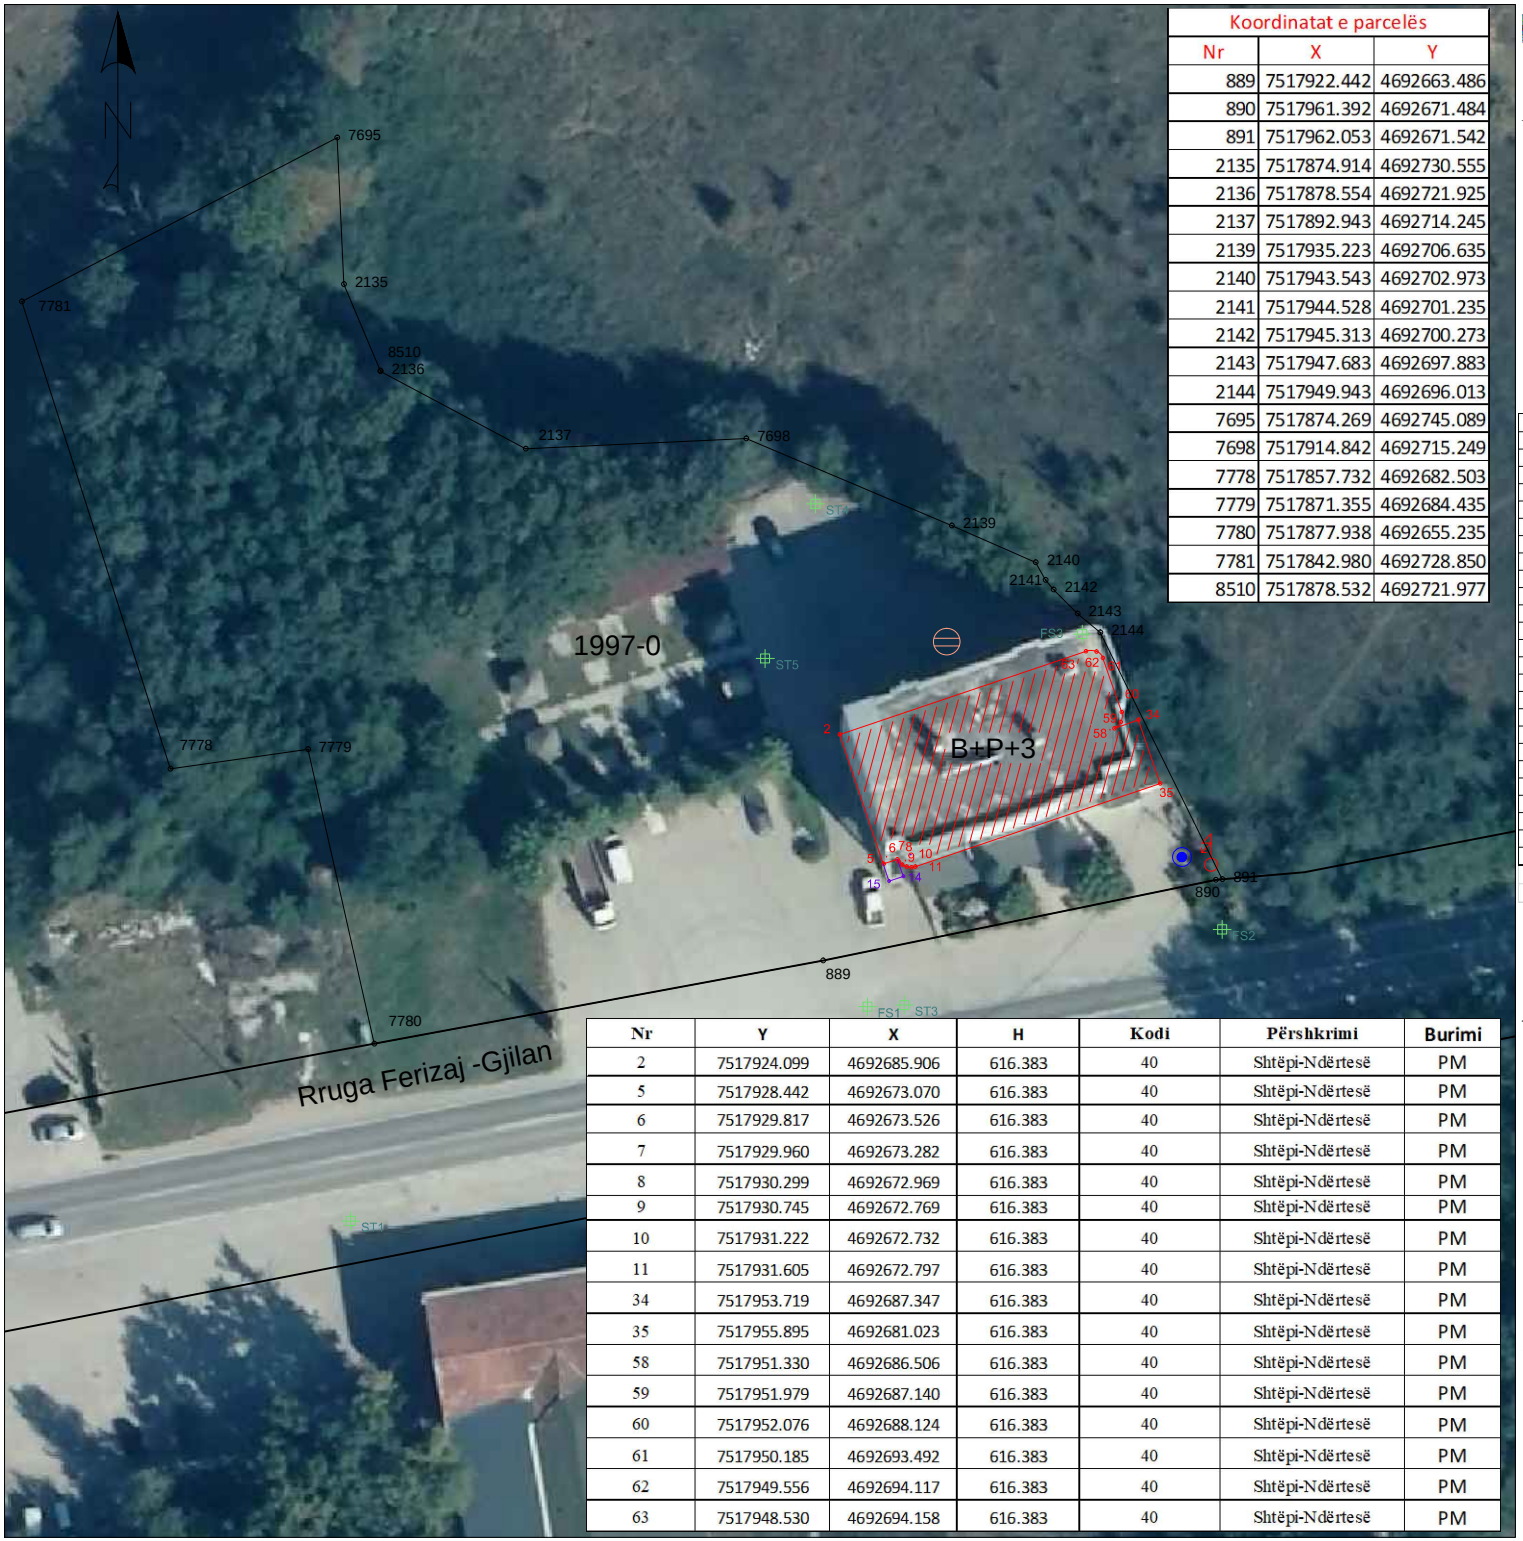

Koordinatat e parcelës		
Nr	X	Y
889	7517922.442	4692663.486
890	7517961.392	4692671.484
891	7517962.053	4692671.542
2135	7517874.914	4692730.555
2136	7517878.554	4692721.925
2137	7517892.943	4692714.245
2139	7517935.223	4692706.635
2140	7517943.543	4692702.973
2141	7517944.528	4692701.235
2142	7517945.313	4692700.273
2143	7517947.683	4692697.883
2144	7517949.943	4692696.013
7695	7517874.269	4692745.089
7698	7517914.842	4692715.249
7778	7517857.732	4692682.503
7779	7517871.355	4692684.435
7780	7517877.938	4692655.235
7781	7517842.980	4692728.850
8510	7517878.532	4692721.977

Nr	Y	X	H	Kodi	Përshkrimi	Burimi
2	7517924.099	4692685.906	616.383	40	Shtëpi-Ndërtesë	PM
5	7517928.442	4692673.070	616.383	40	Shtëpi-Ndërtesë	PM
6	7517929.817	4692673.526	616.383	40	Shtëpi-Ndërtesë	PM
7	7517929.960	4692673.282	616.383	40	Shtëpi-Ndërtesë	PM
8	7517930.299	4692672.969	616.383	40	Shtëpi-Ndërtesë	PM
9	7517930.745	4692672.769	616.383	40	Shtëpi-Ndërtesë	PM
10	7517931.222	4692672.732	616.383	40	Shtëpi-Ndërtesë	PM
11	7517931.605	4692672.797	616.383	40	Shtëpi-Ndërtesë	PM
34	7517953.719	4692687.347	616.383	40	Shtëpi-Ndërtesë	PM
35	7517955.895	4692681.023	616.383	40	Shtëpi-Ndërtesë	PM
58	7517951.330	4692686.506	616.383	40	Shtëpi-Ndërtesë	PM
59	7517951.979	4692687.140	616.383	40	Shtëpi-Ndërtesë	PM
60	7517952.076	4692688.124	616.383	40	Shtëpi-Ndërtesë	PM
61	7517950.185	4692693.492	616.383	40	Shtëpi-Ndërtesë	PM
62	7517949.556	4692694.117	616.383	40	Shtëpi-Ndërtesë	PM
63	7517948.530	4692694.158	616.383	40	Shtëpi-Ndërtesë	PM

Republika e Kosovës

Qeveria -Vlada

Ministria e Mjedisit dhe Planifikimit Hapësinr /Ministarstv Sredine i Prstrng Planiranja

AGJENCIA KADASTRALE E KOSOVËS/ KATASTARSKA AGENCIJA KOSOVA

Situacioni i terrenit

Orto 2018

Zyra kadastrale kmunale / pštinska katastarska kancelarija: Ferizaj

Zona kadastrale / Katastarska zona: Sojevë

Nr. i njësisë kadastrale / Br. katastarske jedinice : 1997-0

Numri i lëndës / Broj predmeta: _____

Shkalla e zvoglimit / Razmera plana 1: 750

Lista e koordinatave të pikave të matura:

Nr	Y	X	H	DSC
1	7517924.161	4692685.901	613.572	BODRUM
3	7517926.768	4692678.123	614.535	BODRUM
4	7517928.821	4692678.788	613.937	BODRUM
12	7517930.512	4692675.687	615.150	BODRUM
13	7517931.532	4692672.775	615.232	BODRUM
55	7517924.191	4692685.892	614.555	BODRUM
56	7517948.520	4692694.153	611.867	BODRUM
57	7517951.216	4692686.498	615.257	BODRUM
70	7517926.875	4692658.909	614.915	FS1
75	7517962.043	4692666.573	615.883	FS2
76	7517948.155	4692695.850	611.884	FS3
71	7517928.446	4692673.114	618.843	K1
72	7517928.451	4692673.056	622.863	K2
73	7517931.362	4692672.636	625.724	K3
74	7517931.362	4692672.636	628.539	K4
41	7517949.257	4692678.690	622.461	KATI1
42	7517950.425	4692677.882	622.236	KATI1
43	7517953.785	4692679.083	621.049	KATI1
21	7517928.456	4692673.049	623.463	KATI2
22	7517936.054	4692675.600	625.415	KATI2
23	7517936.503	4692674.331	624.980	KATI2
24	7517941.000	4692675.531	622.884	KATI2
25	7517945.976	4692677.452	628.719	KATI2
44	7517945.996	4692677.487	627.049	KATI2
45	7517945.550	4692678.782	628.191	KATI2

Nr	Y	X	H	DSC
46	7517953.066	4692681.297	626.976	KATI2
47	7517951.321	4692686.436	626.376	KATI2
48	7517952.036	4692687.127	625.700	KATI2
49	7517952.066	4692688.058	625.669	KATI2
50	7517950.816	4692691.732	628.762	KATI2
51	7517950.181	4692693.521	628.767	KATI2
26	7517929.831	4692673.503	625.706	KATI2-TERASA
27	7517930.223	4692672.985	625.719	KATI2-TERASA
28	7517930.804	4692672.675	625.734	KATI2-TERASA
29	7517931.355	4692672.630	625.735	KATI2-TERASA
30	7517936.482	4692674.384	625.775	KATI2-TERASA
52	7517945.976	4692677.564	625.725	KATI2-TERASA
53	7517950.388	4692679.028	625.731	KATI2-TERASA
54	7517949.930	4692680.269	628.551	KATI2-TERASA
31	7517924.066	4692685.855	628.747	KATI-NK
32	7517926.736	4692678.030	630.525	KATI-NK
33	7517927.188	4692678.173	631.116	KATI-NK
39	7517958.032	4692673.736	615.808	KYQJE-UJSJELLES
64	7517934.710	4692695.099	611.806	PUSET-FEKAL
14	7517930.407	4692671.815	616.383	SHKALET
15	7517928.991	4692671.369	616.383	SHKALET
40	7517960.936	4692672.964	620.759	SHTYLL-ELEKTRIKE
65	7517875.607	4692637.654	614.324	ST1
66	7517993.006	4692670.018	616.453	ST2
67	7517930.523	4692659.075	615.009	ST3
68	7517921.7	4692708.79	611.478	ST4
69	7517916.72	4692693.44	611.772	ST5

Shpjegues:

- Kufiri kadastral (nga SIKTK-G)
- Ndërtesa në trajtim për legalizim
- Ndërtesa tjera
- Aneks Ndërtimi
- Shtyllë elektrike
- Pusetë e ujësjellësit
- Pusetë e ujërave të zeza
- Shkallët
- Pikë e objekteve fqinje
- Rr. Emri i rrugës
- P4 Pikë e rrjetës gjeodezike
- 81 Pikë e shkallëve
- 81 Pikë e terasës
- 10 Pikë e objektit
- Pikë e murit
- 92 Pikë e kulmit

Rilevoi / Snimi: LIRIDON SEJDIU

(emri dhe mbiemri i gjedetit/kompanisë/ ime i prezime gedeta/ kompanije)

Nr. i licencës / Br. licence: 140

Data e rilevimit / Datum snimanja: 21.07.2020

Nënshkrimi / Potpis: _____

V.V.